ARCHITECTURAL DRAWINGS

SHEET NO.	DWG. NO.		SHEET NO.	DWG. NO.		SC.
0 - GENERAL						
	----	COVER SHEET				NTS
00	A-0 00	LIST OF DRAWINGS				NTS
ARCHITECTURAL DRAWINGS						
1 - PLANS						
01	A-1 00	KEY PLAN				
02	A-1 01	BUILDING PLAN				
03	A-1 02	FURNITURE LAYOUT				
04	A-1 03	CEILING LAYOUT				
05	A-1 04	LIGHTING LAYOUT				
06	A-1 05	FLOORING LAYOUT				
2 - ELEVATIONS						
07	A-2 01	ELEVATIONS A				
08	A-2 02	ELEVATIONS B				
3 - SECTIONS						
09	A-3 01	SECTION A				
10	A-3 02	SECTION B				
11	A-3 03	SECTION C				
12	A-3 04	SECTION D				
13	A-3 05	SECTION E & F				

■ List Of Drawings

DRAWING TITLE

- List Of Drawings

PROJECT:	SALES CENTER
UNIT NAME:	IDEAL BUILDING
UNIT NM:	.....
REVISION NM:	
DATE:	15-03-2026

SEVEN SEAS
FOR DEVELOPMENT & INVESTMENT

CLIENT :
IDEAL BUILDING

Designed by :

Shop Drawing by:
eng : MOHAMED ZEIN

Aproved by executive depart :

Final Aprove by :
eng : MOHAMED ZEIN

Revision : 02

Date : 31-03-2026 | Scale: | A-0 00
sheet N.

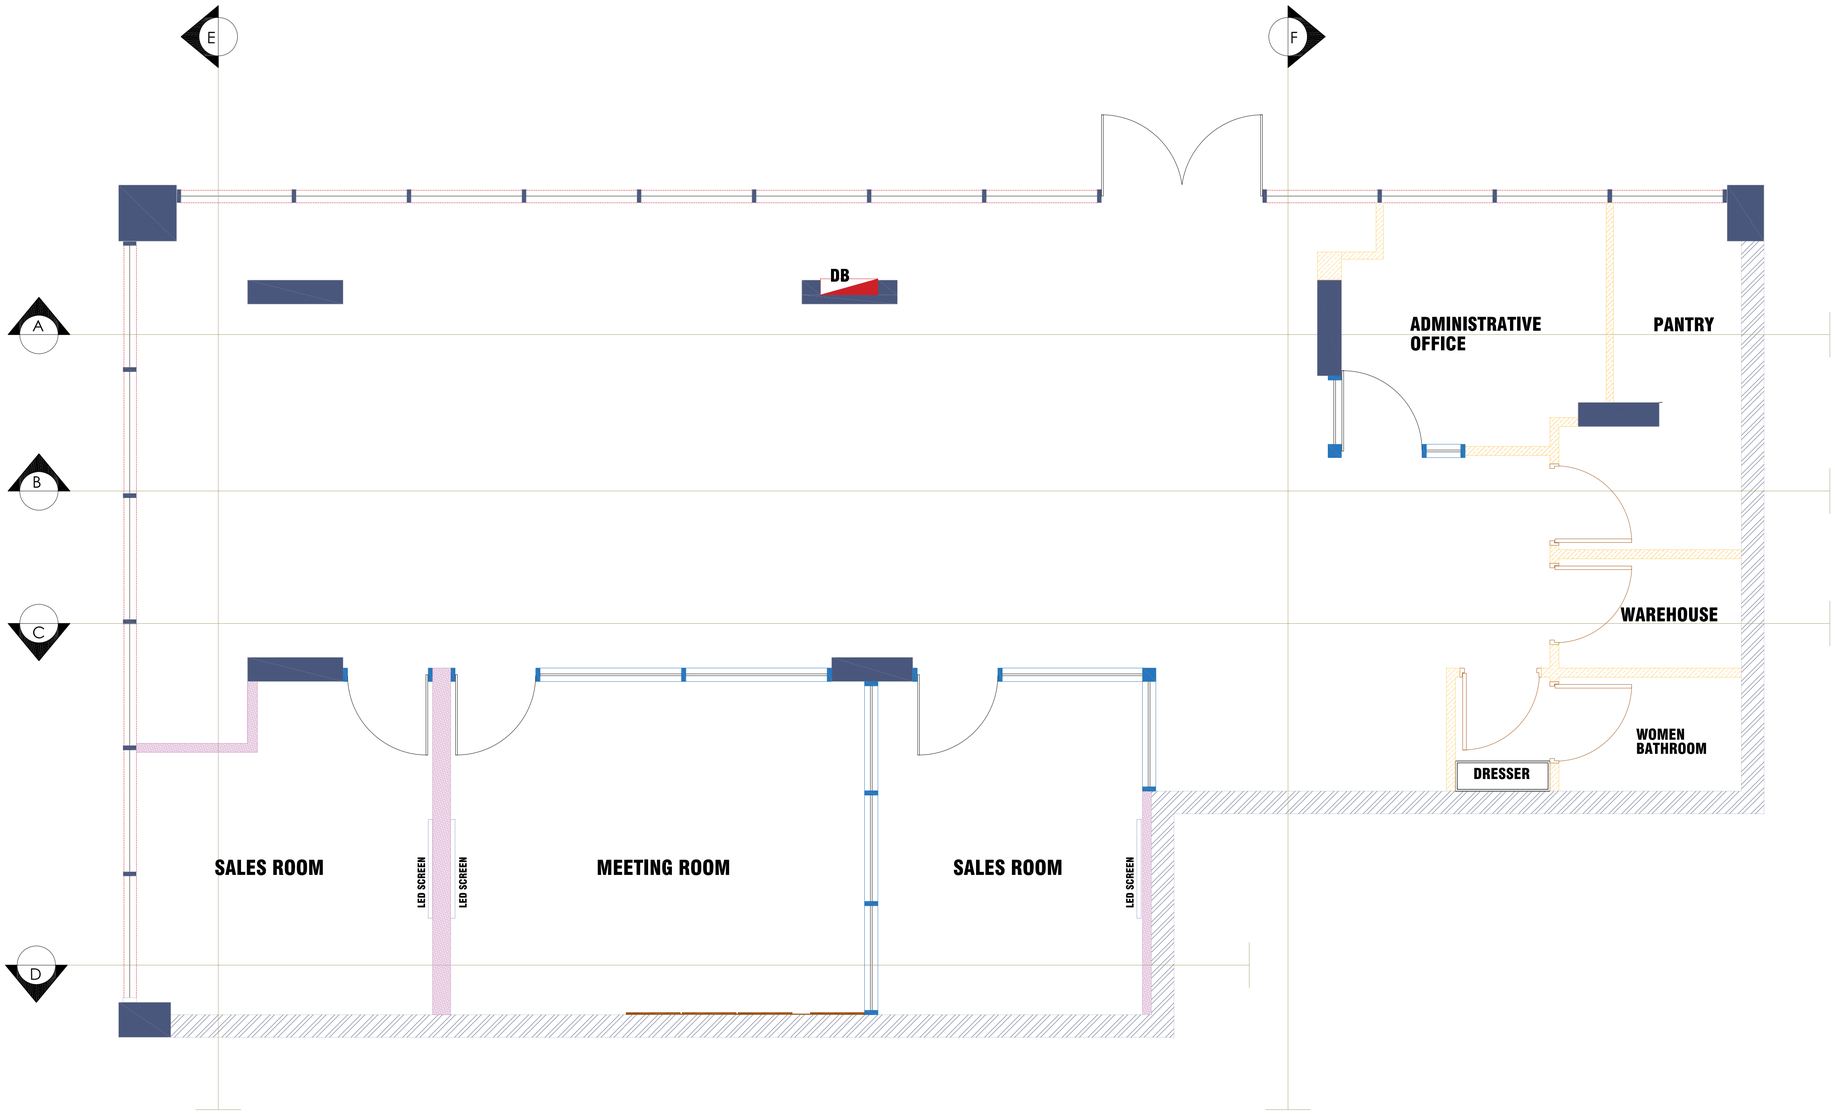

- KEY PLAN

DRAWING TITLE

- KEY PLAN

PROJECT:	SALES CENTER
UNIT NAME:	SALES CENTER
UNIT NM:	0000
REVISION NM:	REVISION NM:
DATE:	15-03-2026

SEVEN SEAS
FOR DEVELOPMENT & INVESTMENT

CLIENT :

IDEAL BUILDING

Designed by :

Shop Drawing by:
eng : MOHAMED ZEIN

Aproved by executive depart :

Final Aprove by :
eng : MOHAMED ZEIN

Revision : 01

Date : 31-03-2026	Scale: 1:1000	A-1 00

sheet N.

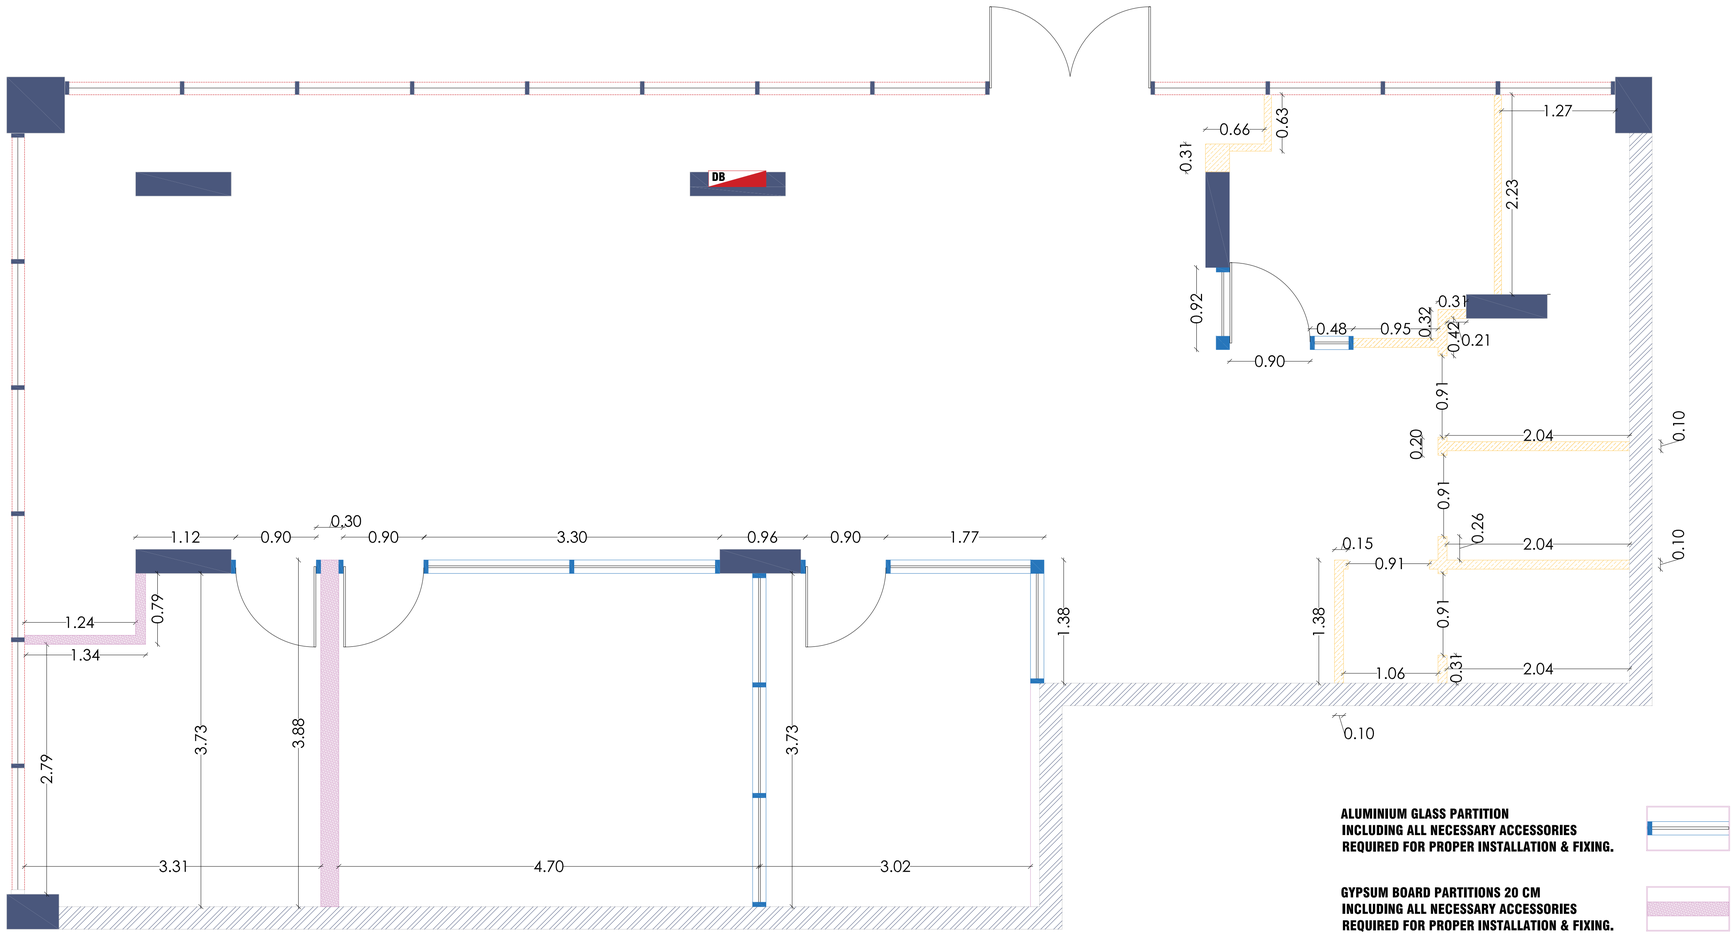

ALUMINIUM GLASS PARTITION
INCLUDING ALL NECESSARY ACCESSORIES
REQUIRED FOR PROPER INSTALLATION & FIXING.

GYPSUM BOARD PARTITIONS 20 CM
INCLUDING ALL NECESSARY ACCESSORIES
REQUIRED FOR PROPER INSTALLATION & FIXING.

CEMENT BOARD PARTITIONS 10 CM
INCLUDING ALL NECESSARY ACCESSORIES
REQUIRED FOR PROPER INSTALLATION & FIXING.

- PARTITIONS LAYOUT

DRAWING TITLE

- PARTITIONS LAYOUT

PROJECT:	SALES CENTER
UNIT NAME:	SALES CENTER
UNIT NM:	0000
REVISION NM:	REVISION NM:
DATE:	15-03-2026

SEVEN SEAS
FOR DEVELOPMENT & INVESTMENT

CLIENT :

IDEAL BUILDING

Designed by :

Shop Drawing by:
eng : MOHAMED ZEIN

Aproved by executive depart :

Final Aprove by :
eng : MOHAMED ZEIN

Revision : 01

Date : 31-03-2026	Scale: 1:1000	A-1 01

sheet N.

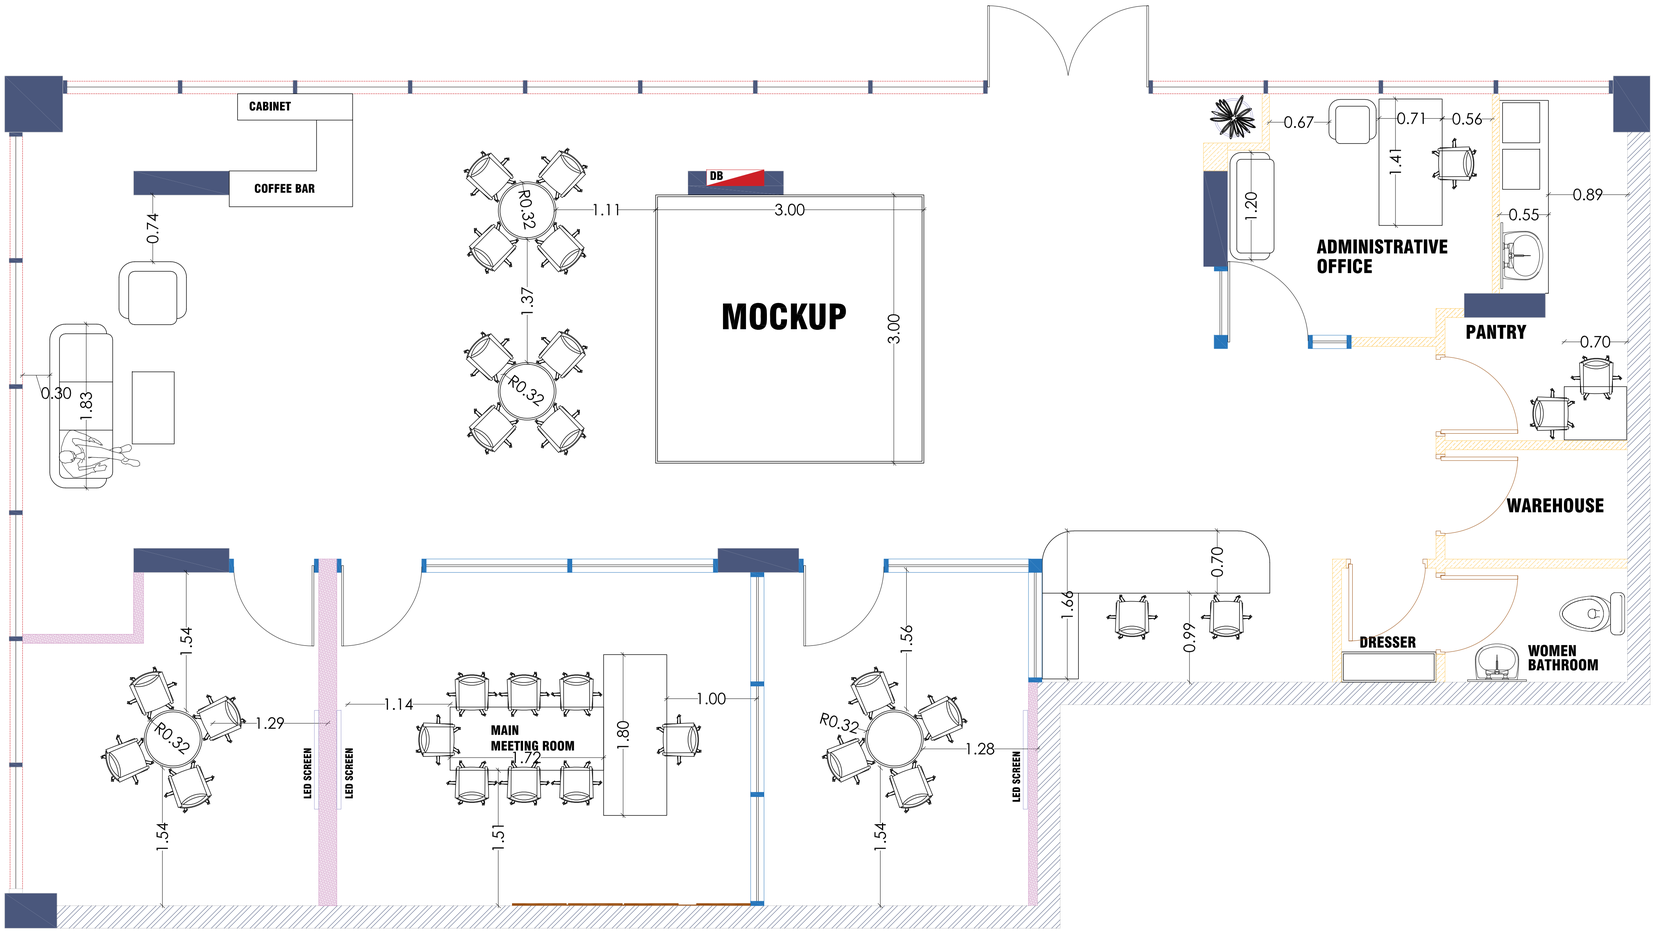

- FURNITURE LAYOUT

DRAWING TITLE

- FURNITURE LAYOUT

PROJECT:	SALES CENTER
UNIT NAME:	SALES CENTER
UNIT NM:	0000
REVISION NM:	REVISION NM:
DATE:	15-03-2026

SEVEN SEAS
FOR DEVELOPMENT & INVESTMENT

CLIENT :

IDEAL BUILDING

Designed by :

Shop Drawing by:
eng : MOHAMED ZEIN

Aproved by executive depart :

Final Aprove by :
eng : MOHAMED ZEIN

Revision : 01

Date : 15-03-2026	Scale: 1:1000	A-1 02

sheet N.

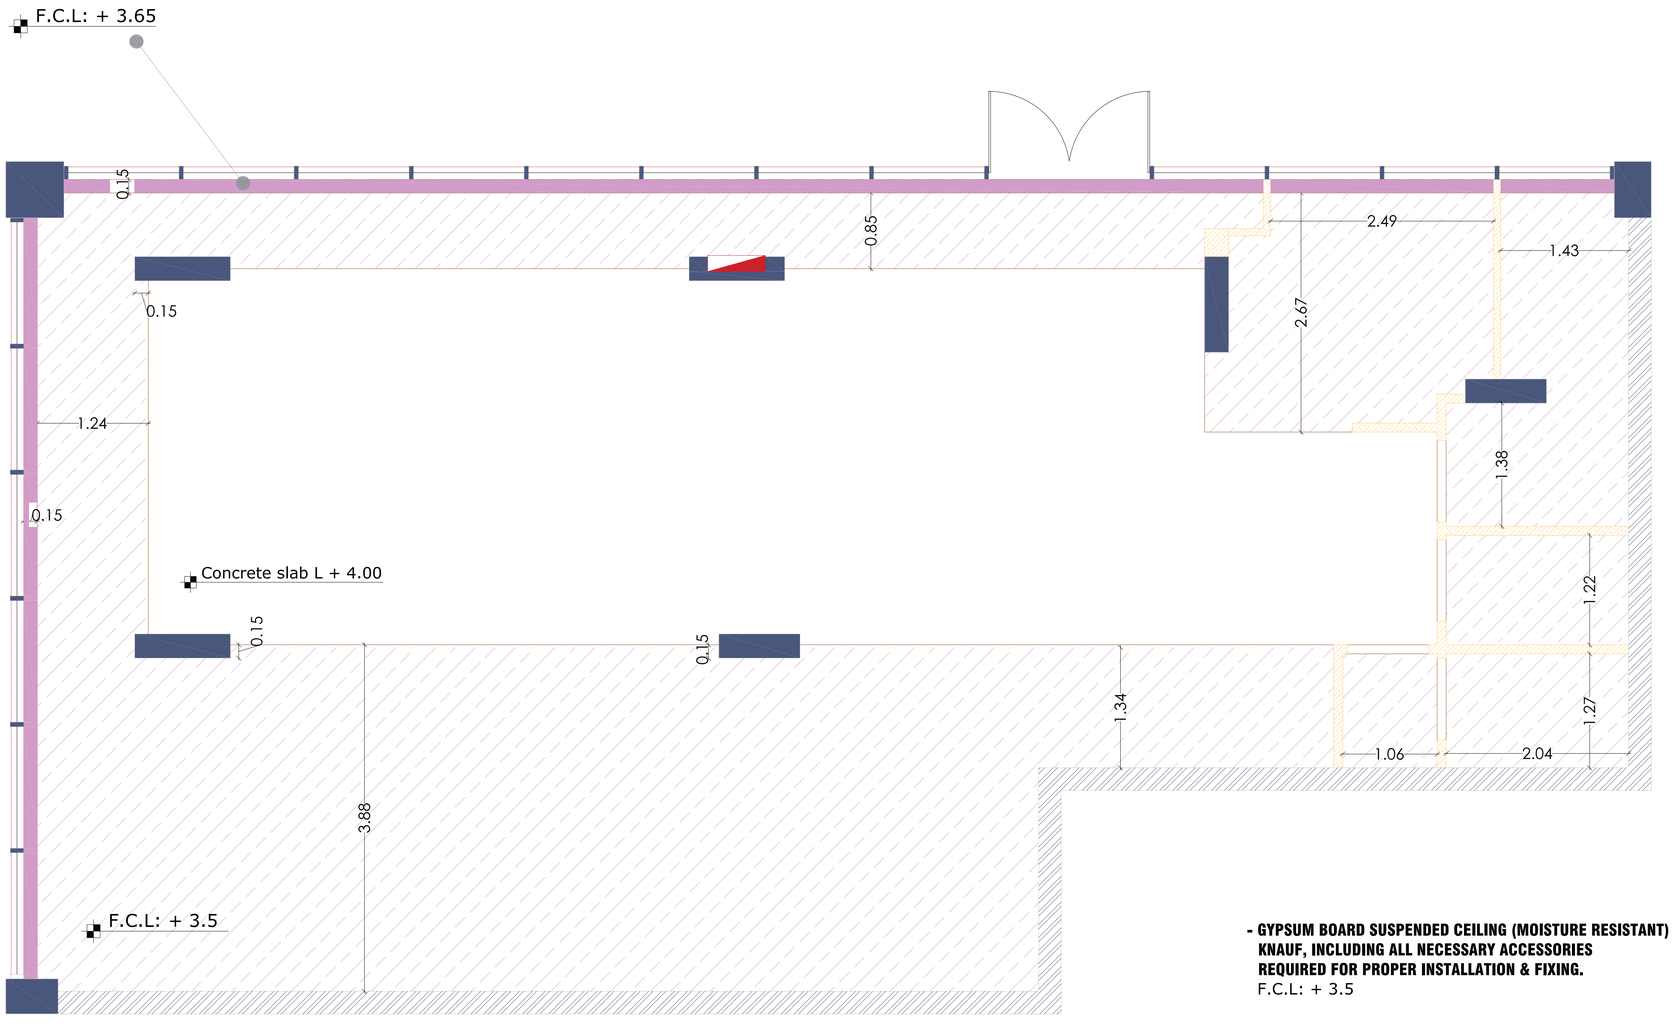

- GYPSUM BOARD SUSPENDED CEILING (MOISTURE RESISTANT) KNAUF, INCLUDING ALL NECESSARY ACCESSORIES REQUIRED FOR PROPER INSTALLATION & FIXING.
F.C.L: + 3.5

- GYPSUM BOARD SUSPENDED CEILING (MOISTURE RESISTANT) KNAUF, INCLUDING ALL NECESSARY ACCESSORIES REQUIRED FOR PROPER INSTALLATION & FIXING.
F.C.L: + 3.65

- CEILING LAYOUT

DRAWING TITLE

- CEILING LAYOUT

PROJECT:	SALES CENTER
UNIT NAME:	SALES CENTER
UNIT NM:	0000
REVISION NM:	REVISION NM:
DATE:	15-03-2026

SEVEN SEAS
FOR DEVELOPMENT & INVESTMENT

CLIENT :

IDEAL BUILDING

Designed by :

Shop Drawing by:
eng : MOHAMED ZEIN

Aproved by executive depart :

Final Aprove by :
eng : MOHAMED ZEIN

Revision : 01

Date : 22-02-2026	Scale: 1:1000	A-1 03

Sheet N.

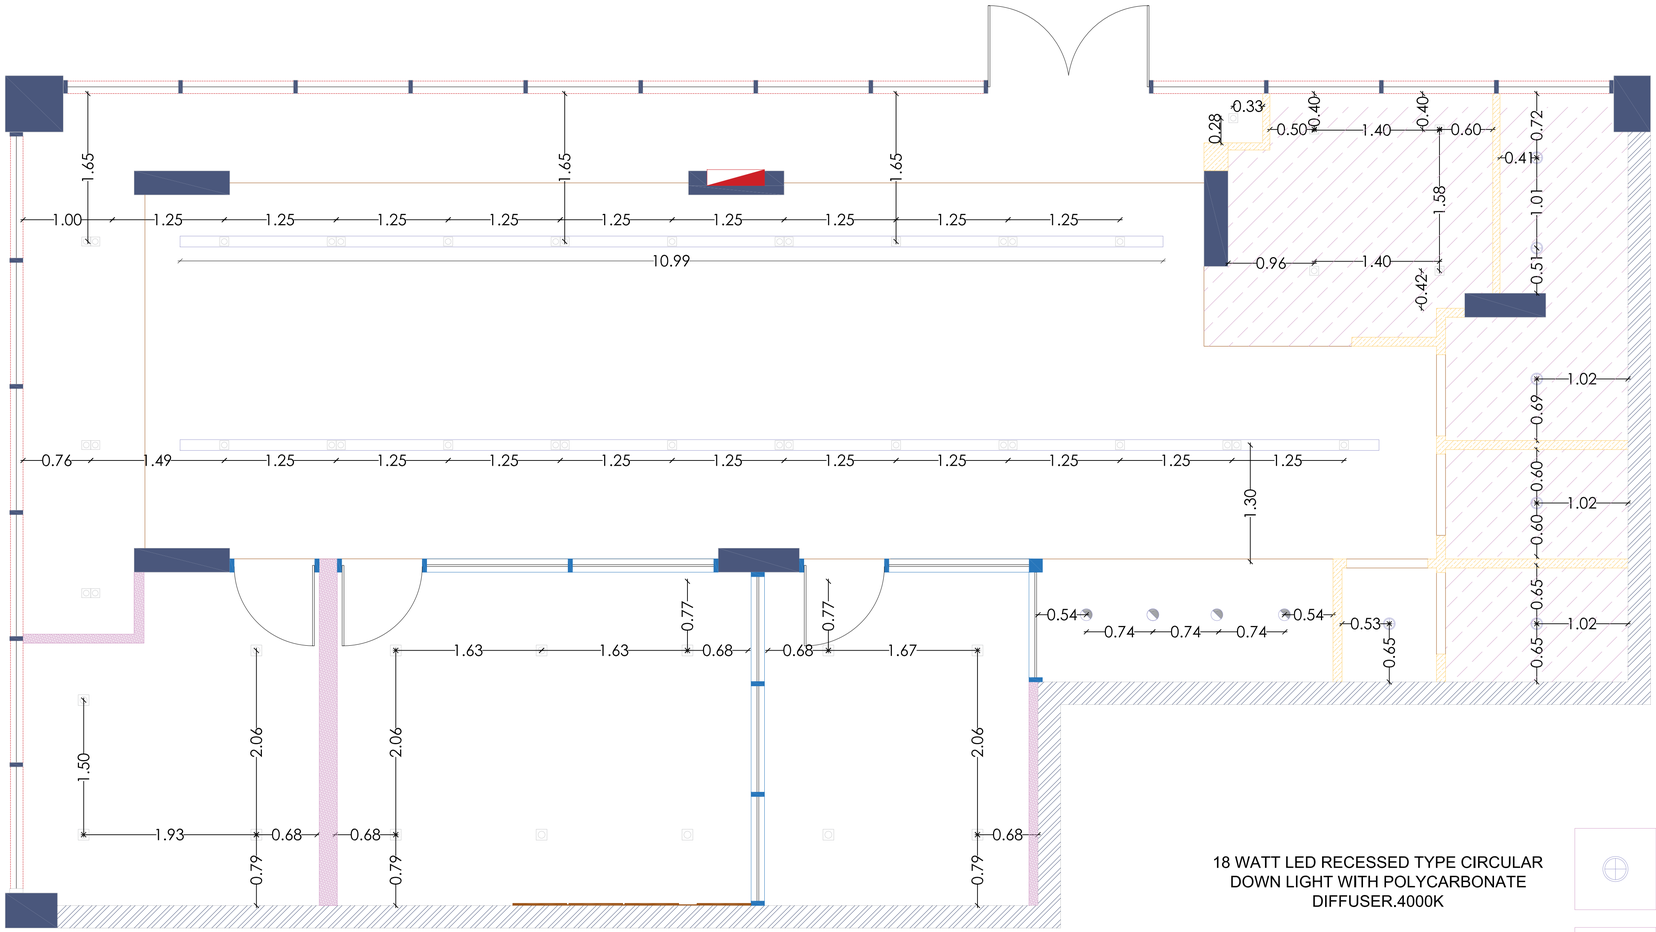

18 WATT LED RECESSED TYPE CIRCULAR DOWN LIGHT WITH POLYCARBONATE DIFFUSER.4000K

24 WATT LED RECESSED TYPE DOWN LIGHT WITH POLY CARBONATE DIFFUSER.4000K - MAGNETIC LIGHTS IN HALL AREA

18 W - PENDANT LIGHT WITH POLY CARBONATE DIFFUSER.4000K

24 WATT LED RECESSED TYPE DOWN LIGHT WITH POLY CARBONATE DIFFUSER.4000K

- LIGHTING LAYOUT

DRAWING TITLE

- LIGHTING LAYOUT

PROJECT:	SALES CENTER
UNIT NAME:	SALES CENTER
UNIT NM:	0000
REVISION NM:	REVISION NM:
DATE:	15-03-2026

SEVEN SEAS
FOR DEVELOPMENT & INVESTMENT

CLIENT :

IDEAL BUILDING

Designed by :

Shop Drawing by:
eng : MOHAMED ZEIN

Aproved by executive depart :

Final Aprove by :
eng : MOHAMED ZEIN

Revision : 01

Date : 15-03-2026	Scale: 1:1000	A-1 04

sheet N.

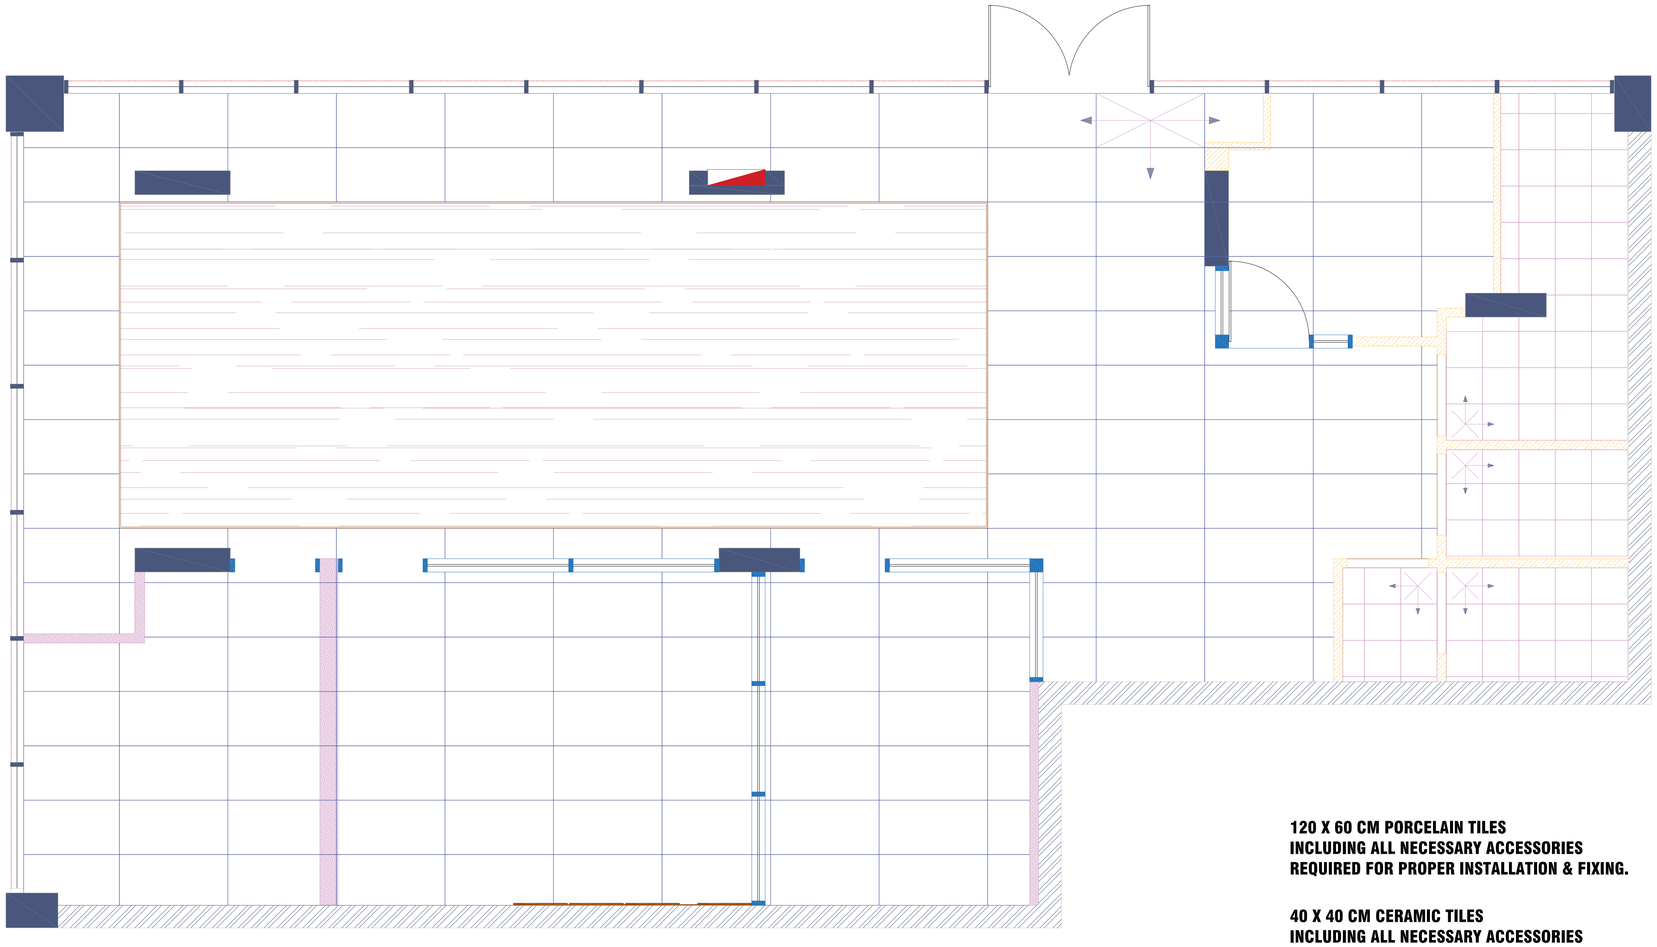

120 X 60 CM PORCELAIN TILES
INCLUDING ALL NECESSARY ACCESSORIES
REQUIRED FOR PROPER INSTALLATION & FIXING.

40 X 40 CM CERAMIC TILES
INCLUDING ALL NECESSARY ACCESSORIES
REQUIRED FOR PROPER INSTALLATION & FIXING.

CARPET AS PER DESIGN

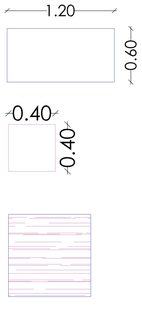

- FLOORING LAYOUT

DRAWING TITLE

- FLOORING LAYOUT

PROJECT:	SALES CENTER
UNIT NAME:	SALES CENTER
UNIT NM:	0000
REVISION NM:	REVISION NM:
DATE:	22-02-2026

SEVEN SEAS
FOR DEVELOPMENT & INVESTMENT

CLIENT :

IDEAL BUILDING

Designed by :

Shop Drawing by:
eng : MOHAMED ZEIN

Aproved by executive depart :

Final Aprove by :
eng : MOHAMED ZEIN

Revision : 01

Date : 22-02-2026	Scale: 1:1000	A-1 05
		sheet N.

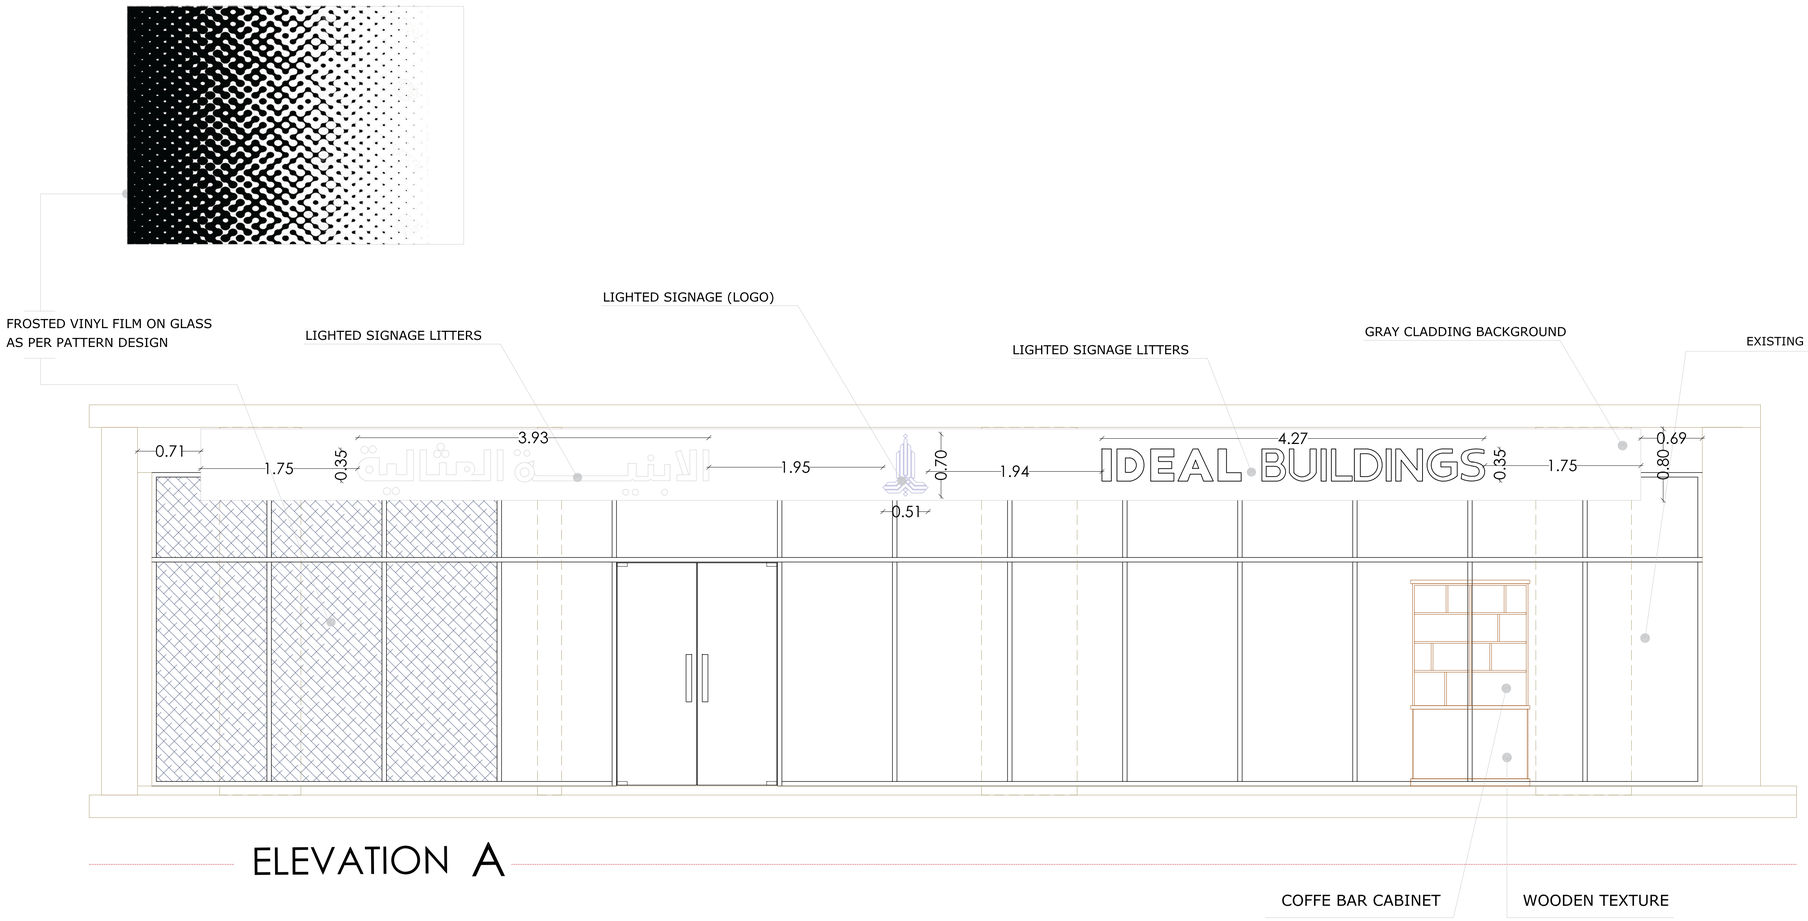

ELEVATION A

DRAWING TITLE

- ELEVATION A

PROJECT:	SALES CENTER
UNIT NAME:	SALES CENTER
UNIT NM:	0000
REVISION NM:	REVISION NM:
DATE:	

SEVEN SEAS
FOR DEVELOPMENT & INVESTMENT

CLIENT :

IDEAL BUILDING

Designed by :

Shop Drawing by:
eng : MOHAMED ZEIN

Aproved by executive depart :

Final Aprove by :
eng : MOHAMED ZEIN

Revision : 02

Date : 31-03-2026	Scale: 1:1000	A-2 01

sheet N.

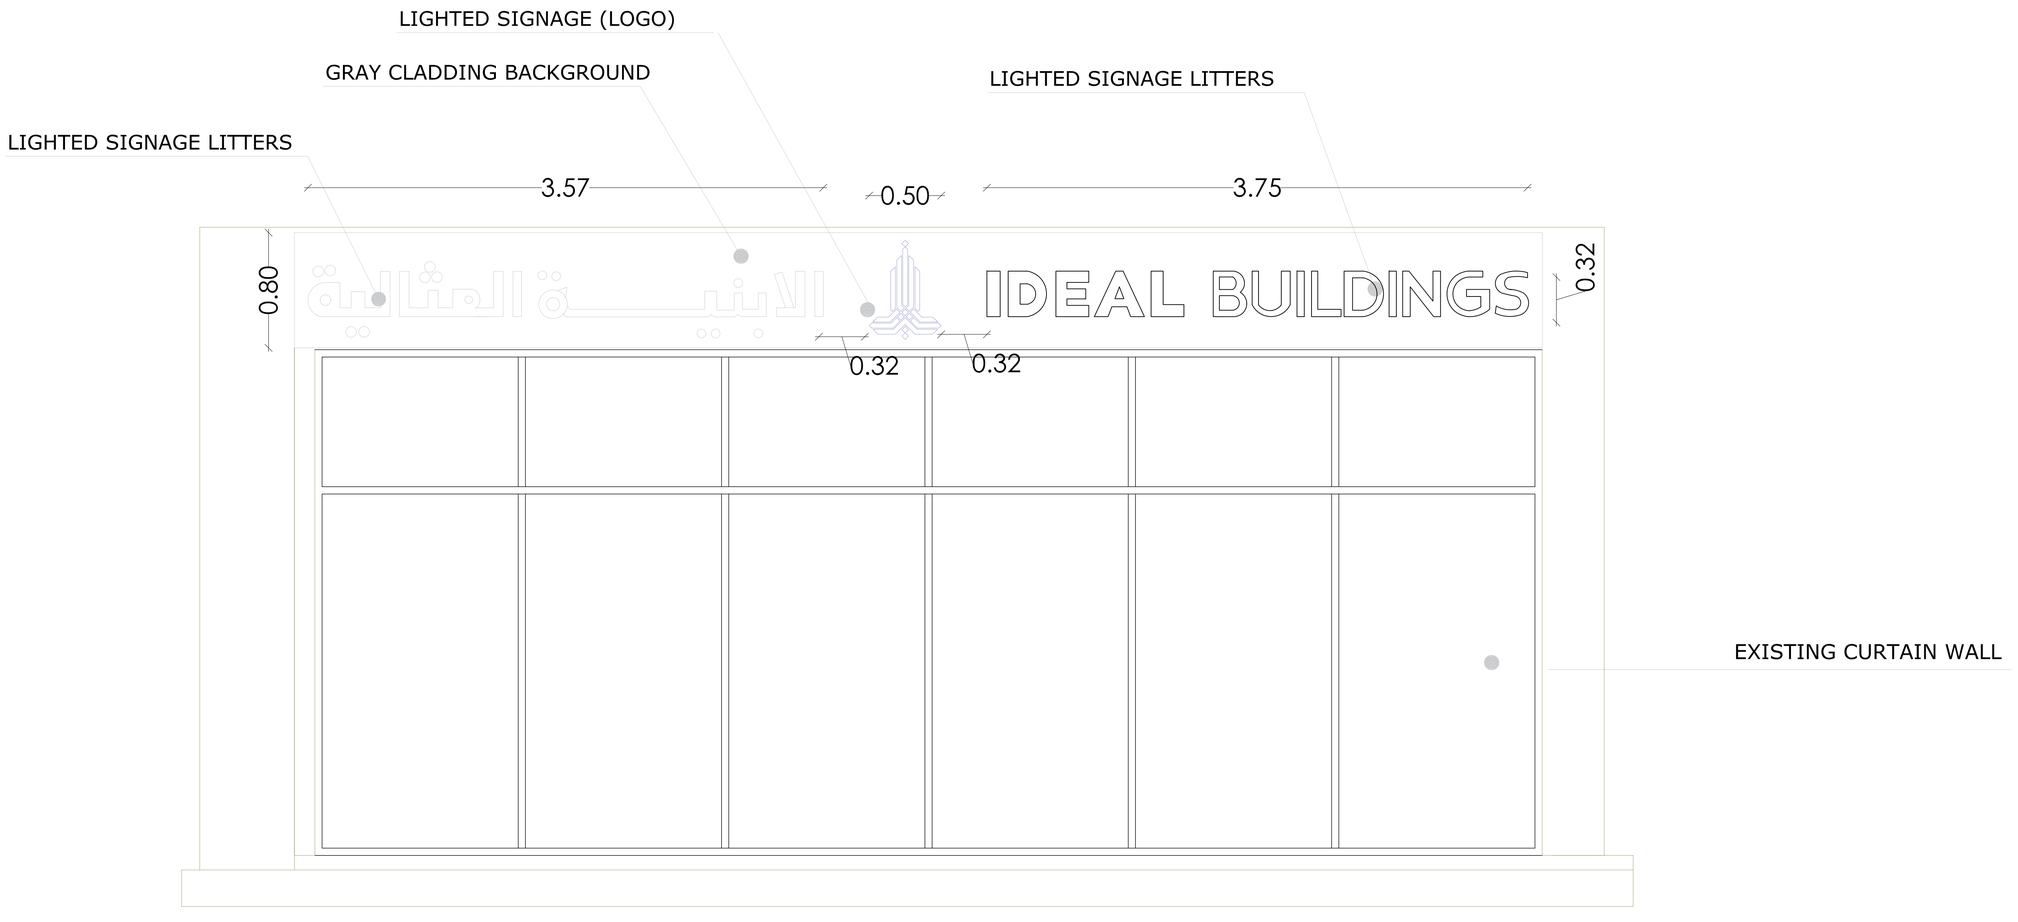

ELEVATION B

ELEVATION B

DRAWING TITLE

- ELEVATION B

PROJECT:	SALES CENTER
UNIT NAME:	SALES CENTER
UNIT NM:	0000
REVISION NM:	REVISION NM:
DATE:	15-03-2026

SEVEN SEAS
FOR DEVELOPMENT & INVESTMENT

CLIENT :

IDEAL BUILDING

Designed by :

Shop Drawing by:
eng : MOHAMED ZEIN

Aproved by executive depart :

Final Aprove by :
eng : MOHAMED ZEIN

Revision : 02

Date :31-03-2026	Scale: 1:1000	A-2 02

sheet N.

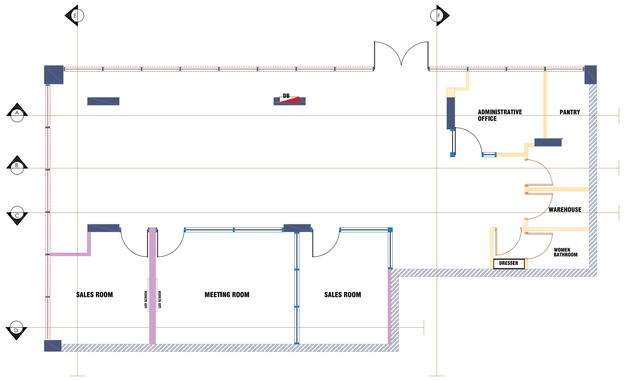

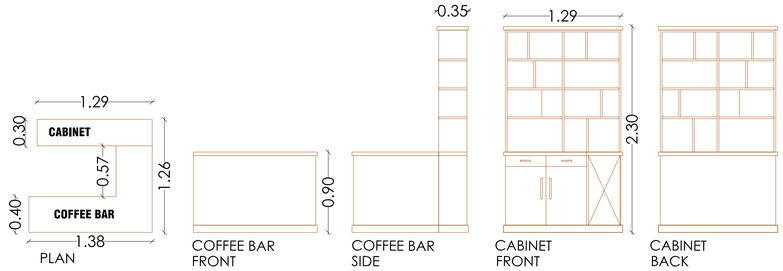

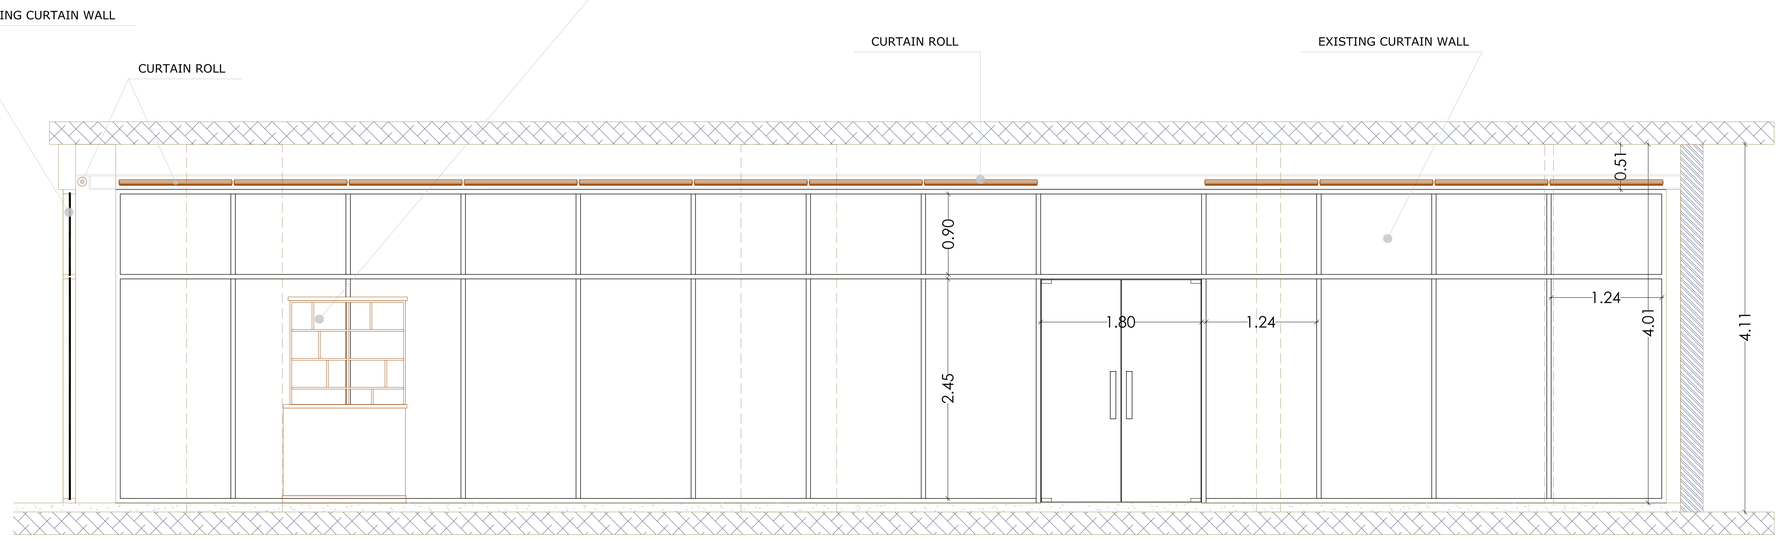

SECTION A

SECTION A

DRAWING TITLE

- SECTION A

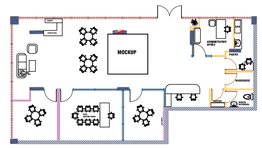

PROJECT:	SALES CENTER
UNIT NAME:	SALES CENTER
UNIT NM:	0000
REVISION NM:	REVISION NM:
DATE:	15-03-2026

SEVEN SEAS
FOR DEVELOPMENT & INVESTMENT

CLIENT :

IDEAL BUILDING

Designed by :

Shop Drawing by:
eng : MOHAMED ZEIN

Aproved by executive depart :

Final Aprove by :
eng : MOHAMED ZEIN

Revision : 02

Date : 31-03-2026	Scale: 1:1000	

sheet N.

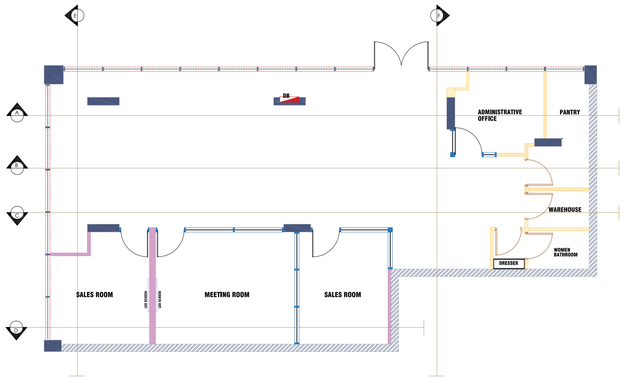

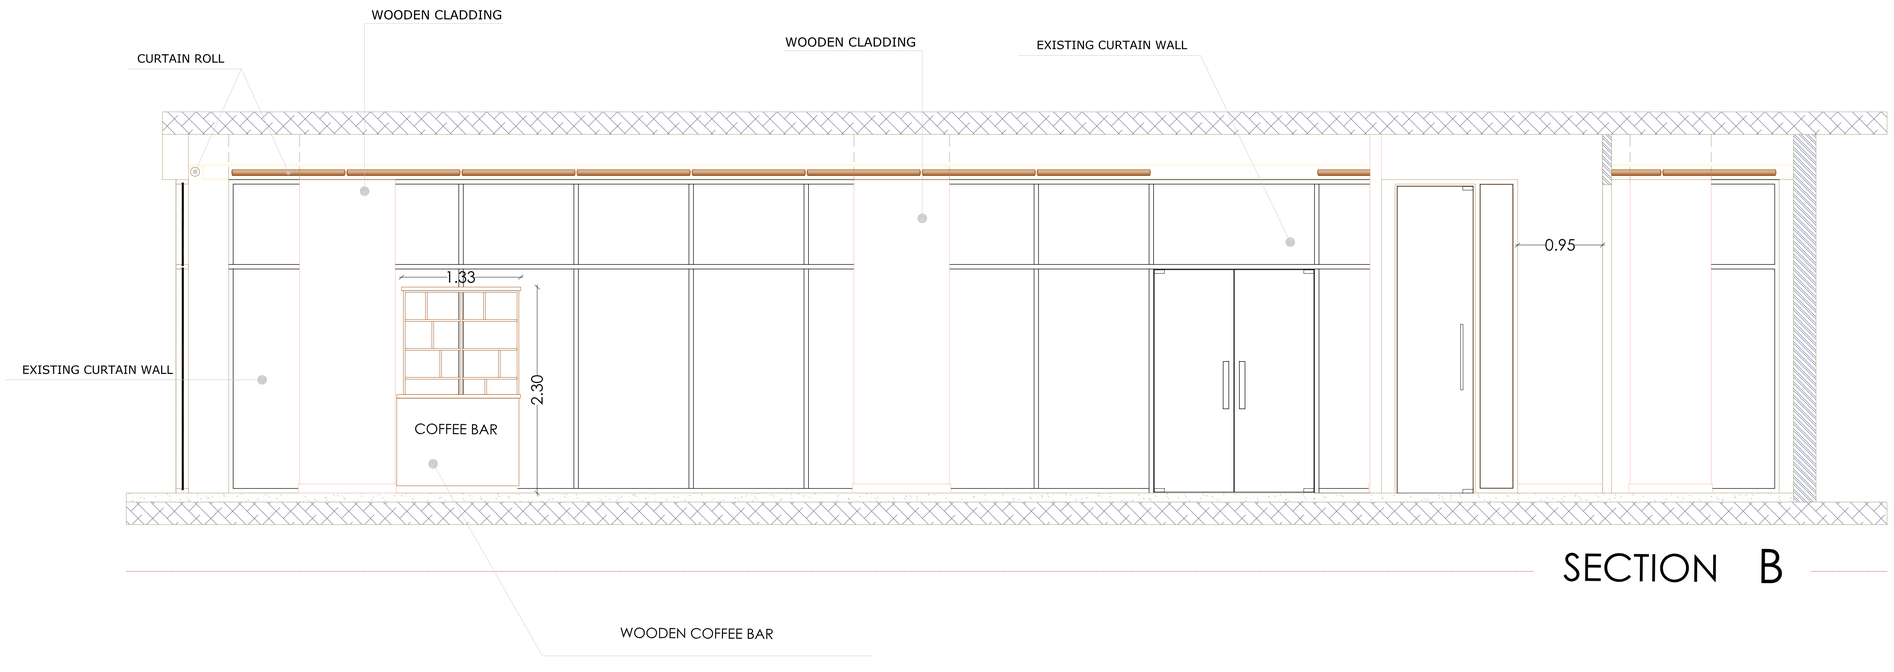

SECTION B

DRAWING TITLE

- SECTION B

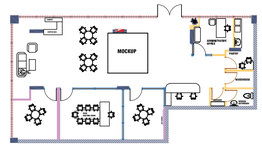

PROJECT:	SALES CENTER
UNIT NAME:	SALES CENTER
UNIT NM:	0000
REVISION NM:	REVISION NM:
DATE:	15-03-2026

SEVEN SEAS
FOR DEVELOPMENT & INVESTMENT

CLIENT :

IDEAL BUILDING

Designed by :

Shop Drawing by:
eng : MOHAMED ZEIN

Aproved by executive depart :

Final Aprove by :
eng : MOHAMED ZEIN

Revision : 02

Date : 31-03-2026	Scale: 1:1000	

sheet N.

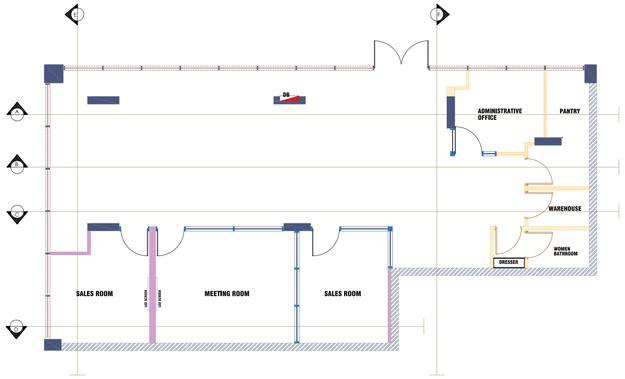

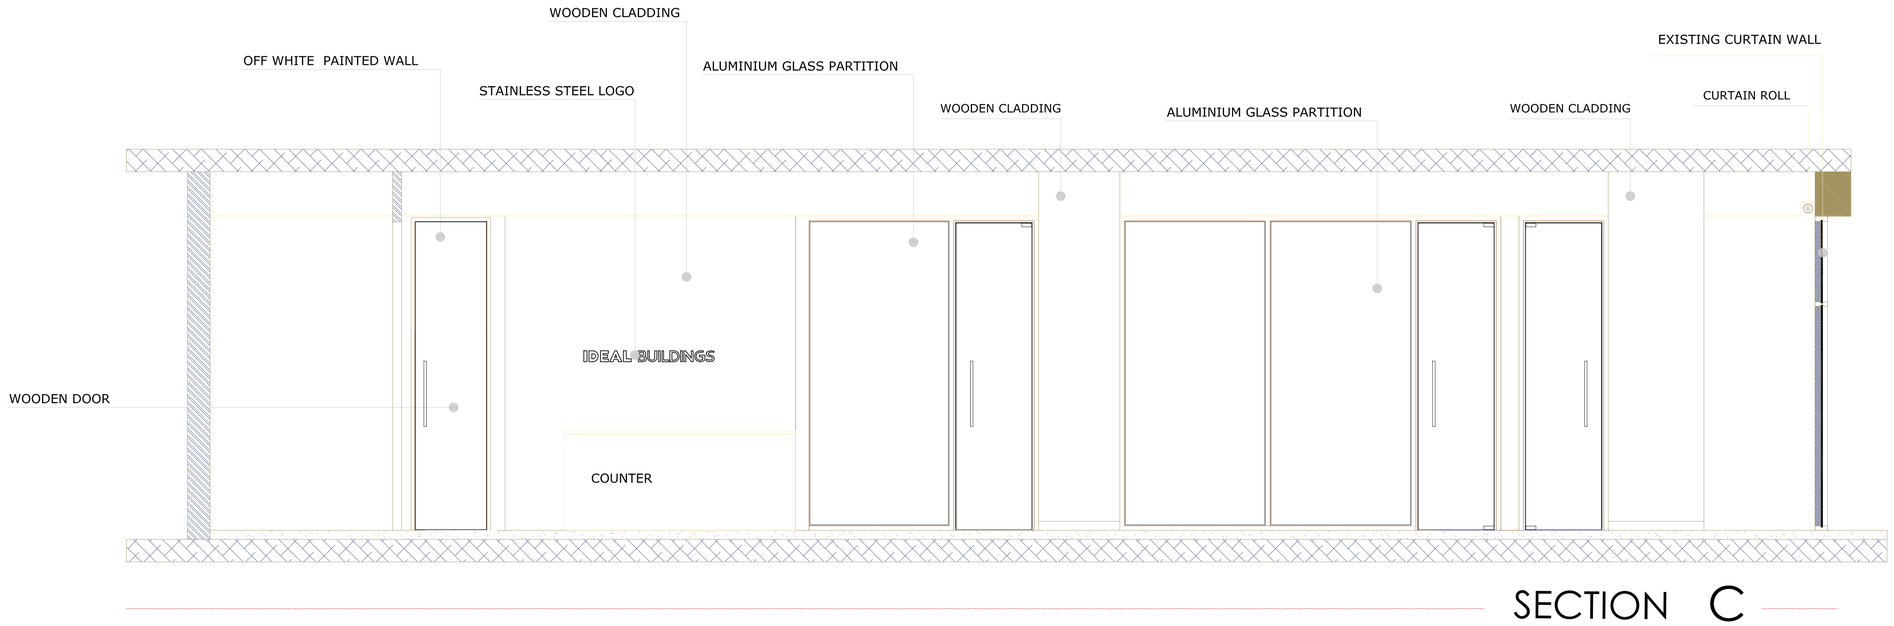

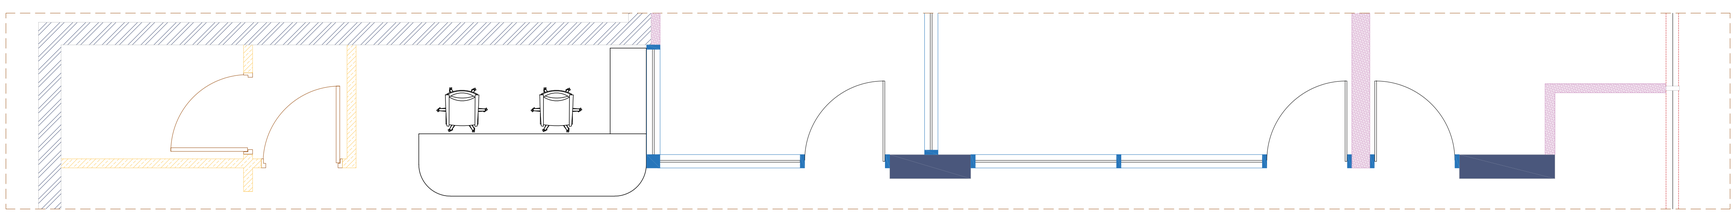

SECTION C

DRAWING TITLE

- SECTION C

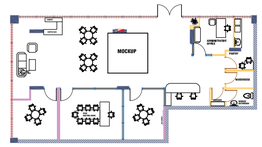

PROJECT:	SALES CENTER
UNIT NAME:	SALES CENTER
UNIT NM:	0000
REVISION NM:	REVISION NM:
DATE:	15-03-2026

SEVEN SEAS
FOR DEVELOPMENT & INVESTMENT

CLIENT :

IDEAL BUILDING

Designed by :

Shop Drawing by:
eng : MOHAMED ZEIN

Aproved by executive depart :

Final Aprove by :
eng : MOHAMED ZEIN

Revision : 02

Date : 31-03-2026	Scale: 1:1000	

sheet N.

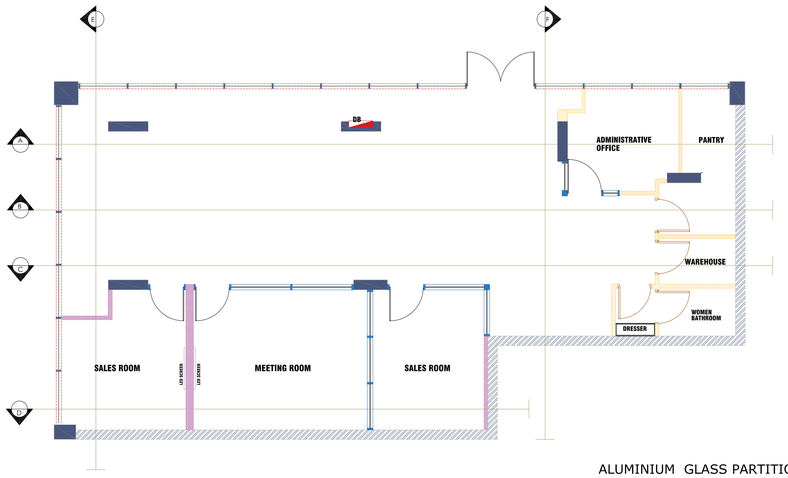

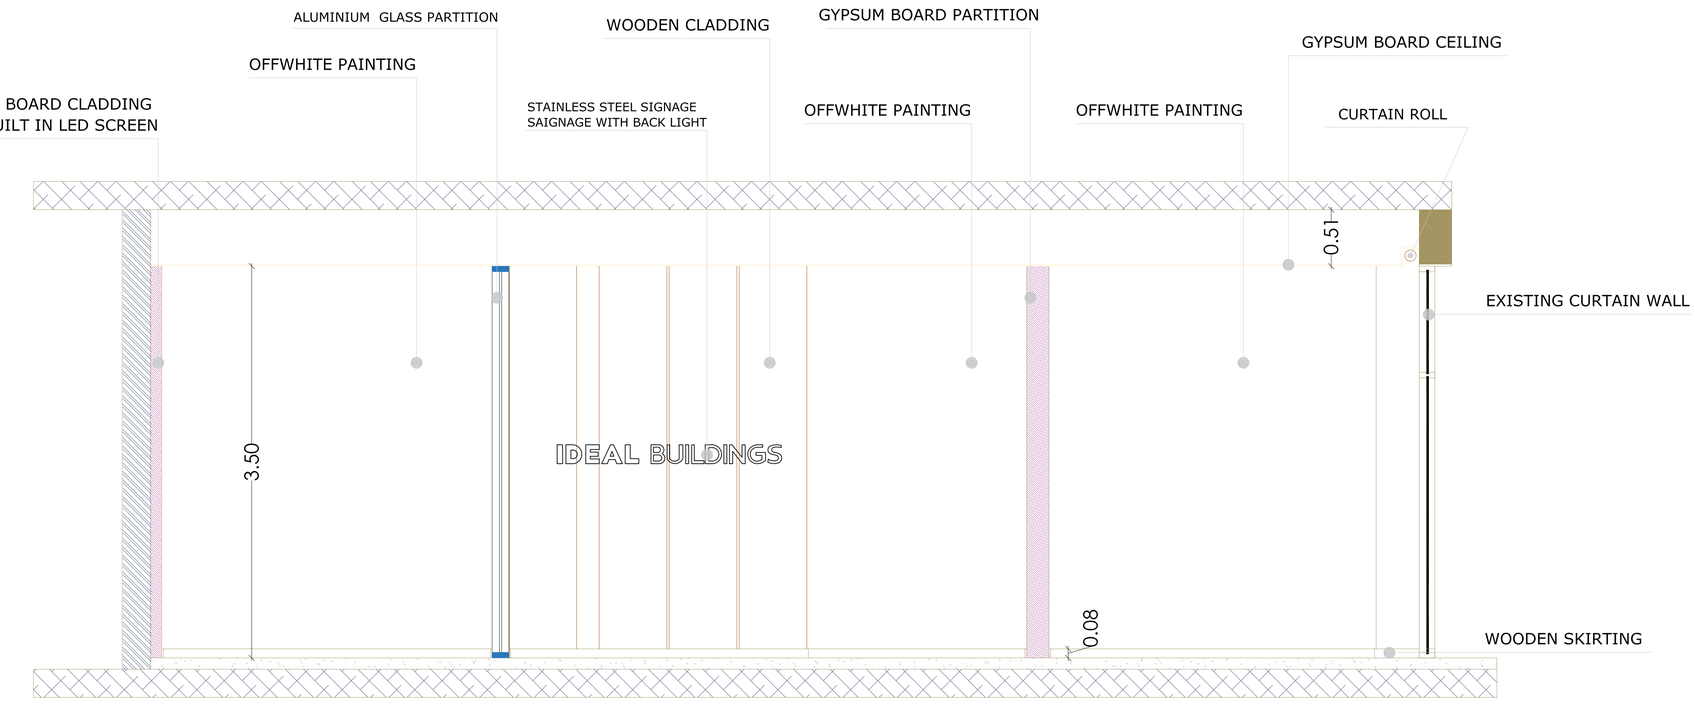

SECTION D

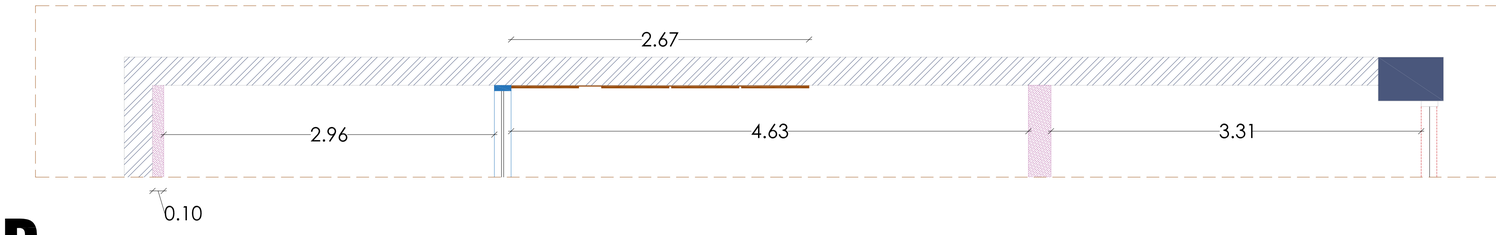

SECTION D

DRAWING TITLE

- SECTION D

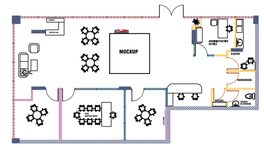

PROJECT:	SALES CENTER
UNIT NAME:	SALES CENTER
UNIT NM:	0000
REVISION NM:	REVISION NM:
DATE:	15-03-2026

SEVEN SEAS
FOR DEVELOPMENT & INVESTMENT

CLIENT :

IDEAL BUILDING

Designed by :

Shop Drawing by:
eng : MOHAMED ZEIN

Aproved by executive depart :

Final Aprove by :
eng : MOHAMED ZEIN

Revision : 02

Date : 31-03-2026 | Scale: 1:1000 | sheet N.

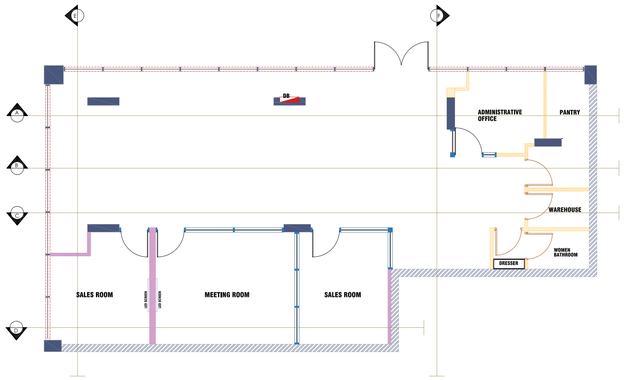

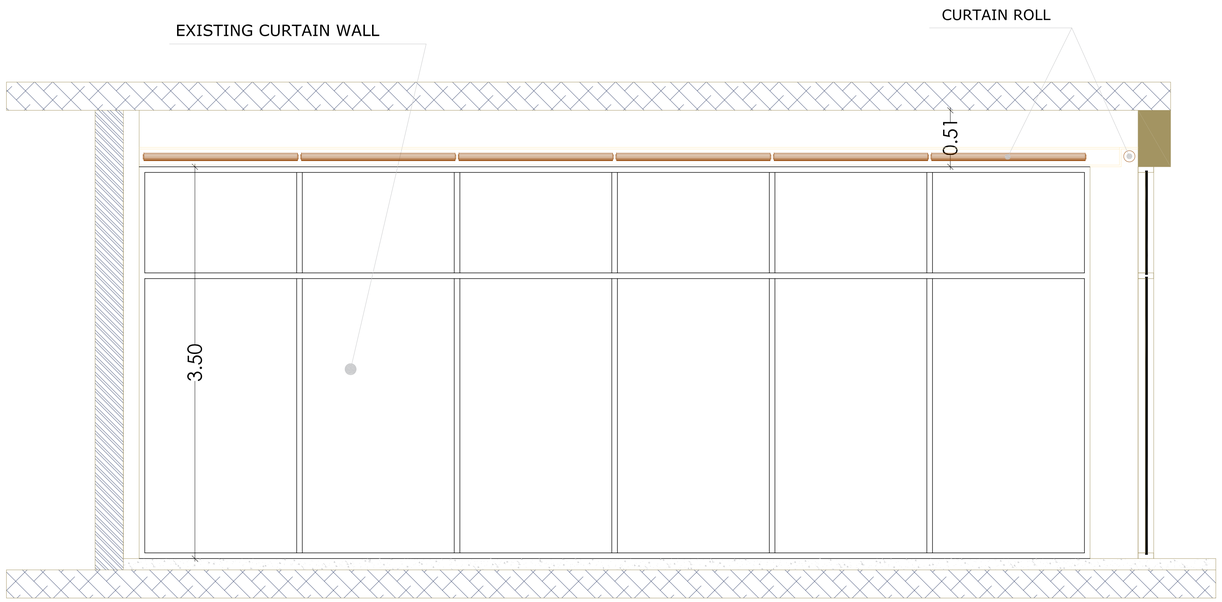

SECTION E

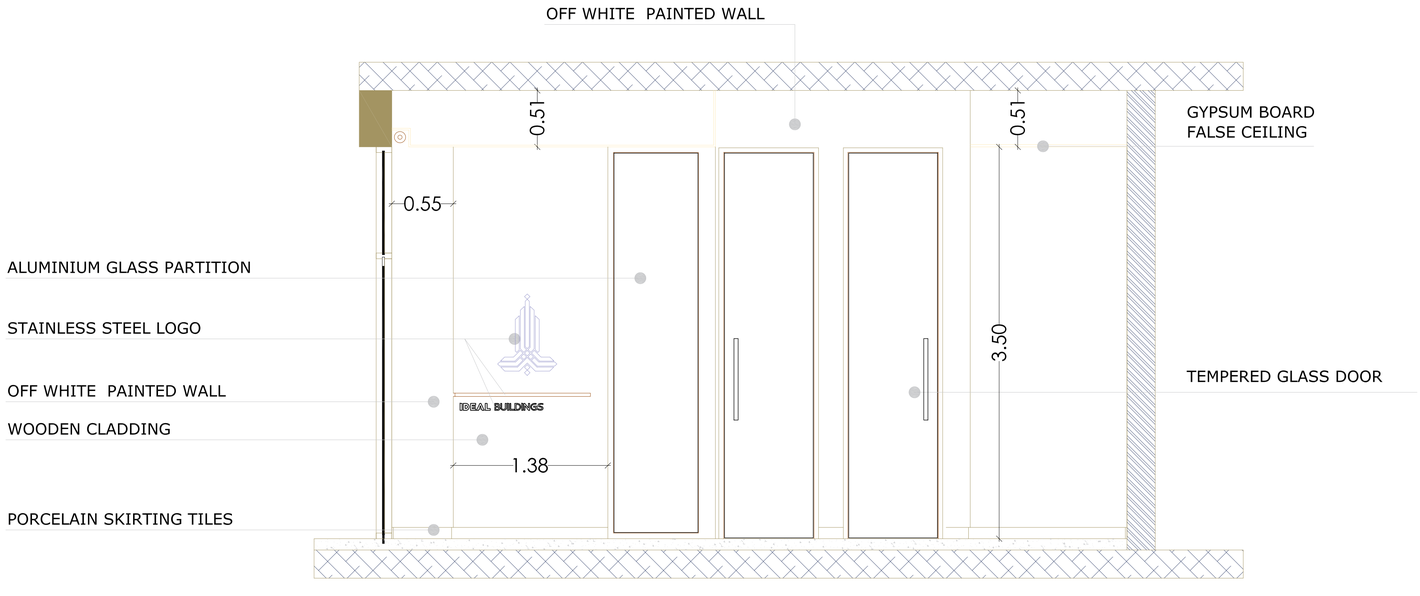

SECTION F

SECTION E & F

DRAWING TITLE

- SECTION E & F

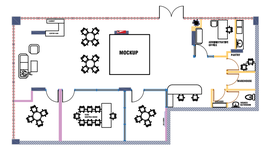

PROJECT:	SALES CENTER
UNIT NAME:	SALES CENTER
UNIT NM:	0000
REVISION NM:	REVISION NM:
DATE:	15-03-2026

SEVEN SEAS
FOR DEVELOPMENT & INVESTMENT

CLIENT :

IDEAL BUILDING

Designed by :

Shop Drawing by:
eng : MOHAMED ZEIN

Aproved by executive depart :

Final Aprove by :
eng : MOHAMED ZEIN

Revision : 02

Date : 31-03-2026	Scale: 1:1000	

sheet N.